
NOTE : STANDARD FASTENER TORQUE AS PER STD-DES-01-00 FR-DES-006-00

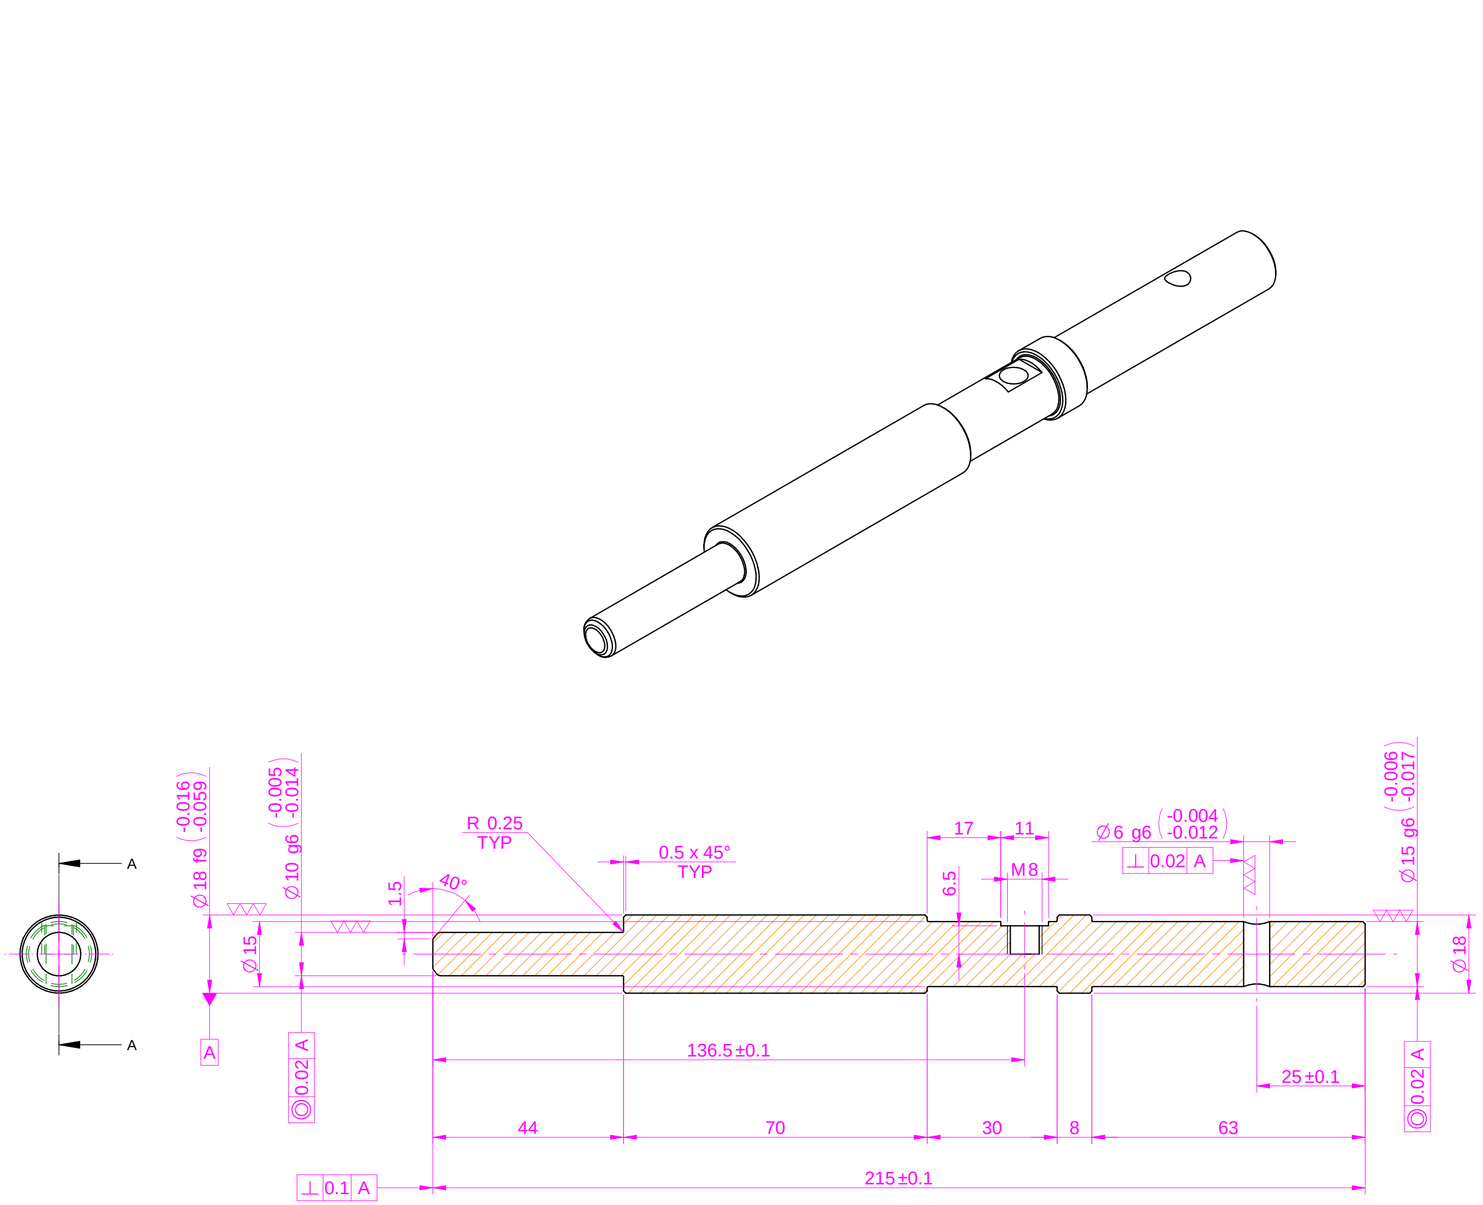

SECTION A-A
SCALE 1:1

HEAT TREATMENT NOTE:-

1) TO BE TOUGHENED UPTO 24-32 HRC.
2) THREADS TO BE KEEP SOFT.
3) RETAPPING TO BE DONE AFTER SURFACE TREATMENT AT SUPPLIER END.(IF APPLICABLE)

NOTE :
MATERIAL : Steel - Unalloyed:1.0503 , C45
FINISH : I.Z.B.P. (TRIVALENT)
MACHINING : ▽▽(▽▽▽)

NOTE:- 1)TO BE TOUGHENED TO 28-30 HRc.
2)REMOVE ALL SHARP EDGES & CORNERS.
3)ALL KEYWAY ARE IN LINE & SHOULD BE DONE IN ONE SETTING.
4) STRAIGHTNESS:- 0.2mm/1000mm MAX.
5) RUNOUT:- 0.1mm/1000mm.

NOTE FOR WIPRO PARI DESIGN -REF. ONLY
WEAR DETAILS : Error: No reference

RESERVED SPACE FOR
CONTROLLED COPY

DEBURR AND REMOVE SHARP EDGES UNLESS SHARP EDGE REQUIREMENT SPECIFIED

UNSP.RADII	UNSP.CHF.
0.5 R	0.5 X 45°

UNSPECIFIED TOL.(FAB) FOR ANGULAR IN mm	
UP TO 10	±1.5°
10 UP TO 50	±0°50'
50 UP TO 120	±0°25'
120 UP TO 400	±0°15'

UNSPECIFIED TOL.(FAB) FOR LINEAR IN mm	
0.5 UP TO 3	±0.1
3 UP TO 6	±0.2
6 UP TO 30	±0.5
30 UP TO 120	±0.8
120 UP TO 315	±1.2
315 UP TO 1000	±2
1000 UP TO 2000	±3
OVER 2000	±4

UNSPECIFIED TOL.(M/C) FOR ANGULAR IN mm	
UP TO 10	±1°
10 UP TO 50	±0°30'
50 UP TO 120	±0°20'
120 UP TO 400	±0°10'

UNSPECIFIED TOL.(M/C) FOR LINEAR IN mm	
0.5 UP TO 3	±0.1
3 UP TO 6	±0.1
6 UP TO 30	±0.2
30 UP TO 120	±0.3
120 UP TO 315	±0.5
315 UP TO 1000	±0.8
1000 UP TO 2000	±1.2
OVER 2000	±2

LIMITS
Gen Tol.: IS 2102

REVISION	DESCRIPTION	DATE	DRN.BY

wipro PARI
www.wipropari.com

1.ALL DIMENSIONS ARE IN mm
2.DO NOT SCALE DRAWING.
3.IF IN DOUBT , ASK TEAM MEMBER
LOCATION : PUNE

© ALL RIGHTS OF REPRODUCTION & DISTRIBUTION ARE RESERVED

WIPRO PARI GROUP

DESCRIPTION: SHAFT-3
DRAWING TYPE: MACHINING

SURFACE AREA	SURFACE TREATMENT	MACHINING	DESIGN UNIT	DESIGN UNIT CD.	TEAM NO.	SHEET SIZE
17.15 in^2	#	#	WPP	0100	PL-01	A2

REFERENCE DWG. ---- | PART CLASS. B | HEAT TREATMENT ----

DRN.BY	CHKD.BY	APPD.BY	MATERIAL	DRG./PART CODE	REV.	SCALE
PCS	NITIN G	SANDEEP J	#	P24DKB014086	00	1 : 1
10/12/2025	10/12/2025	10/12/2025	NET WEIGHT-Kg 0.30 kg			SHEET 1 OF 1

\\srv01101\E:\DM Uploading\2024-25\P24DKP24DKB014086.dft